
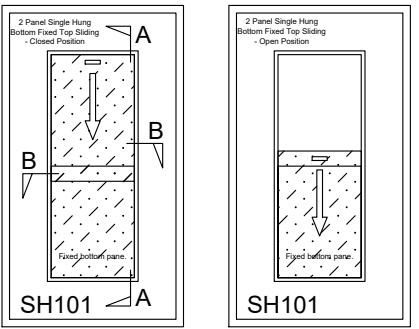
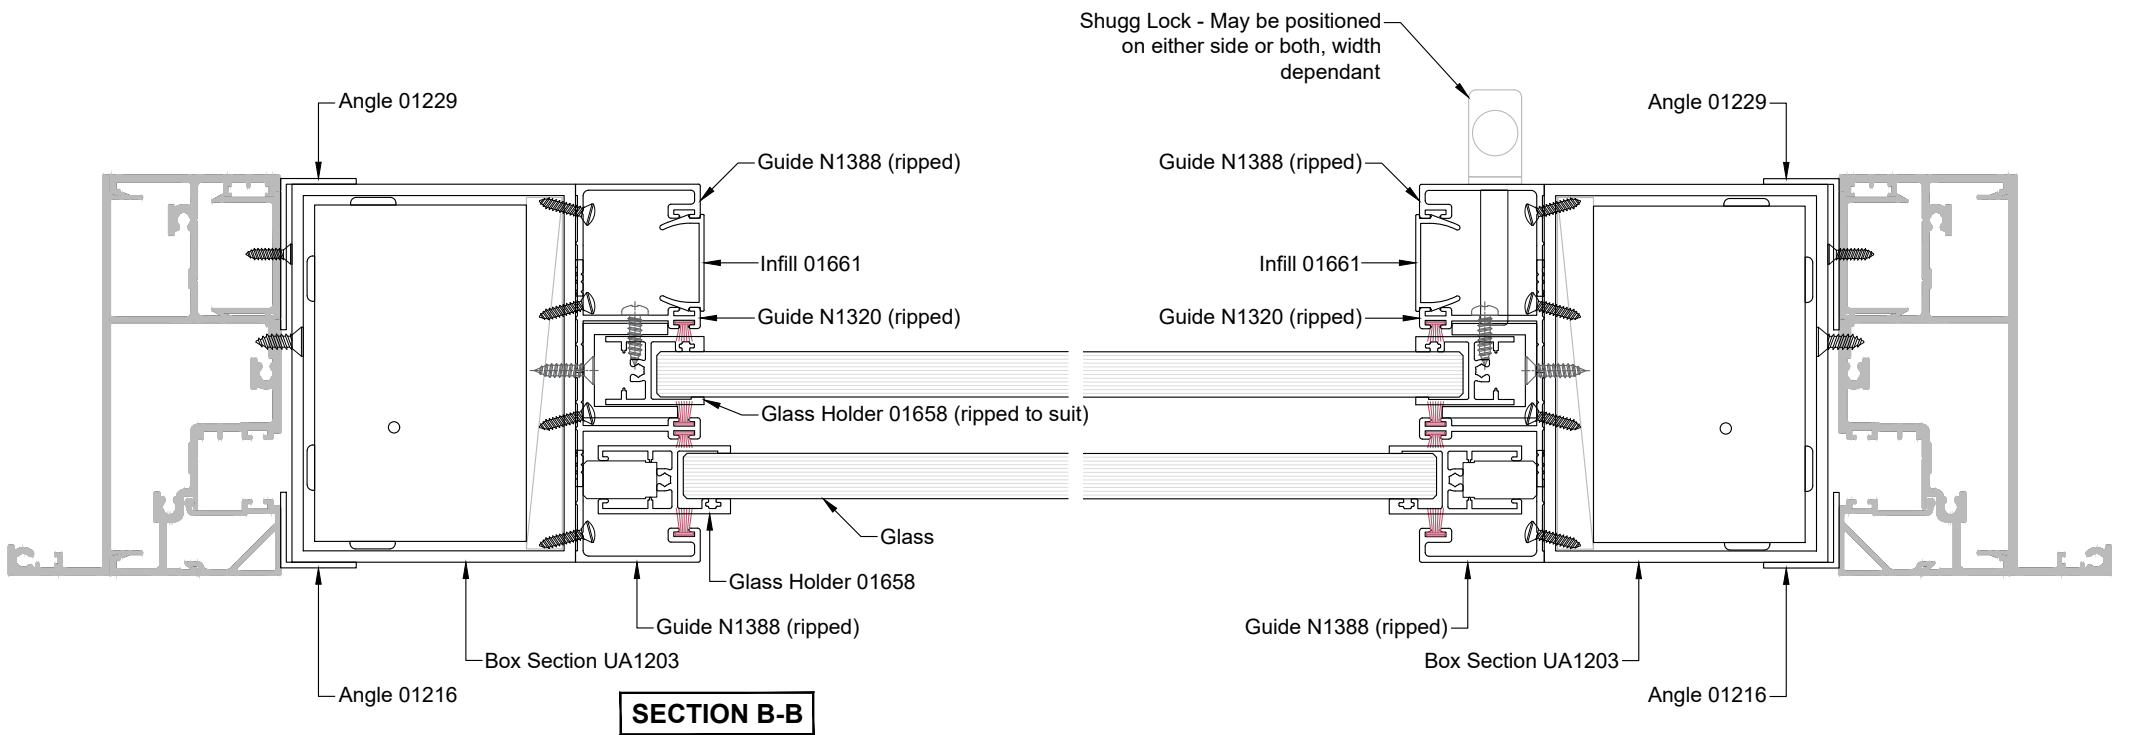
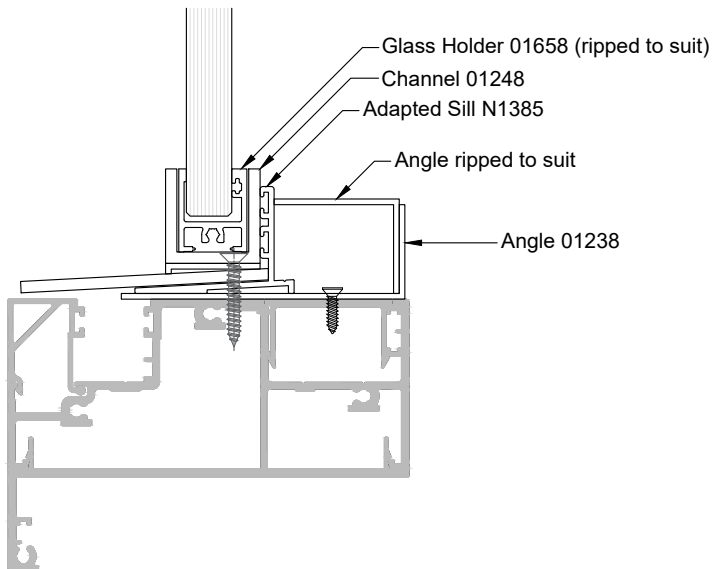
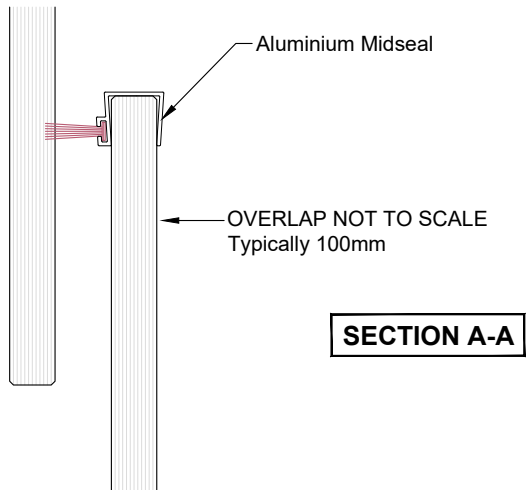


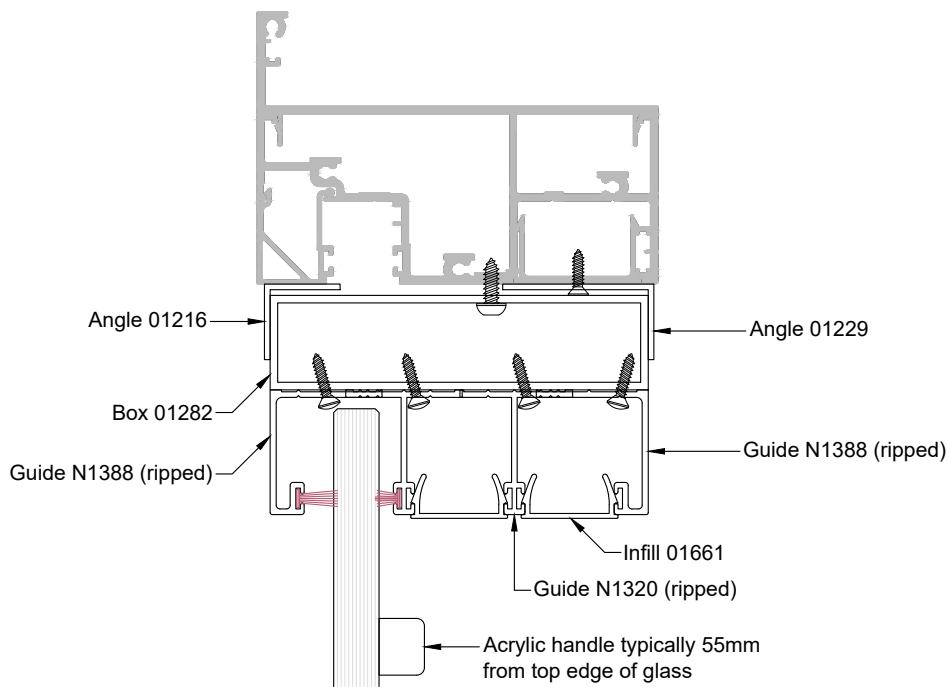

Vertical sliding single hung window Commercial 2 pane bottom fixed Pool Barrier

Features:

- Sashless pane of glass moves within it's own plane
- Bottom fixed pane, top pane slides down
- Provides protection for swimming pools
- No transoms

Specifications:

- Frame height from 1500mm
- Frame width from 1000mm
- Bottom minimum 1200mm high
- Toughened glass panels
- Low E glass options available
- Most powder coated and anodised aluminium finishes available as standard

Neotechnical Industries Ltd
9 McDonald St, Sandringham,
Auckland.
Phone: 09 815 0481
Email: info@shugg.co.nz
www.shugg.co.nz

Frame Type	APL 106 Architectural Casement	Drawing name	SH101-BA4	Scale	1:2 @ A3
Section	A:A & B:B	Date drawn	14-09-21	Revision	001
Notes	-	Window style	Single Hung		
Notes	-	Window format	Commercial Pool Barrier		
Notes	-	Glazing	Single	Thickness	12mm

Details subject to change without notice. Exterior frames by others, Neotechnical Industries Ltd does not own the rights to exterior frames shown and are indicative only. All other details
© Neotechnical Industries Ltd, not to be reproduced, altered or distributed in any form without permission.